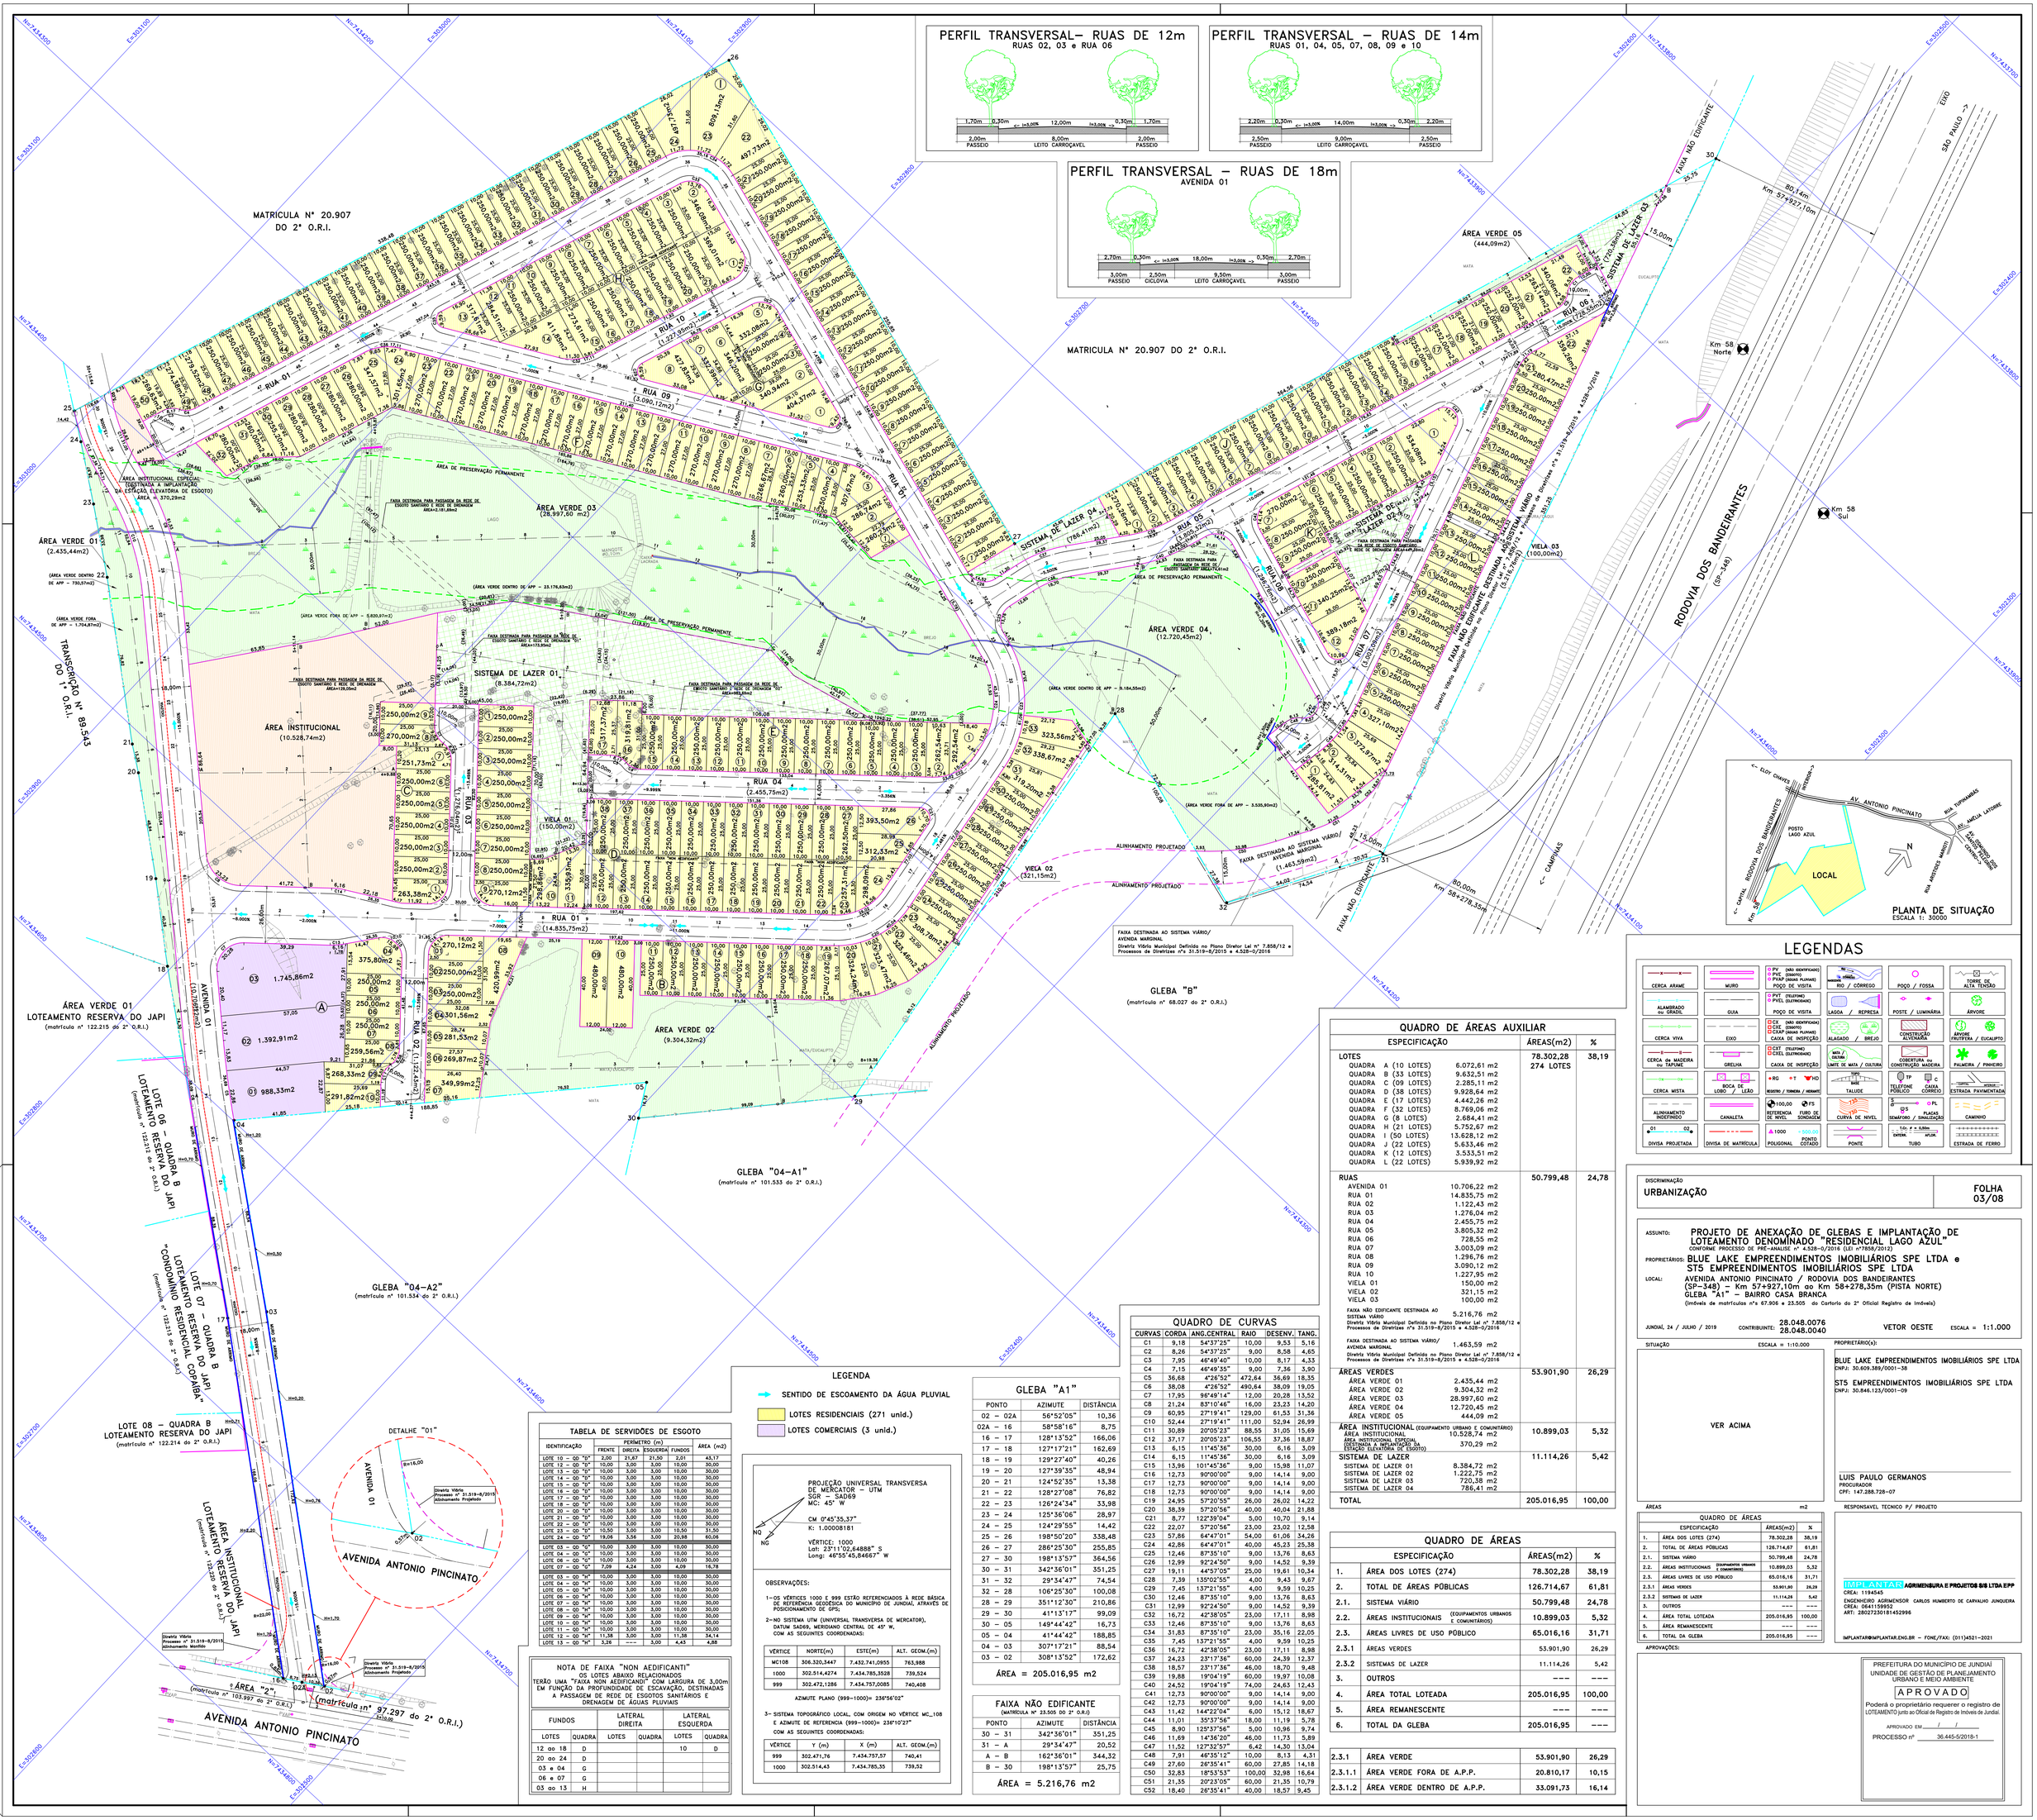


PONTO	AZIMUTE	DISTÂNCIA
02 – 02A	56°52'05"	10,36
02A – 16	58°58'16"	8,75
16 – 17	128°13'52"	166,06
17 – 18	127°17'21"	162,69
18 – 19	129°27'40"	40,26
19 – 20	127°39'35"	48,94
20 – 21	124°52'35"	13,38
21 – 22	128°27'08"	76,82
22 – 23	126°24'34"	33,98
23 – 24	125°36'06"	28,97
24 – 25	124°29'55"	14,42
25 – 26	198°50'20"	338,48
26 – 27	286°25'30"	255,85
27 – 30	198°13'57"	364,56
30 – 31	342°36'01"	351,25
31 – 32	29°34'47"	74,54
32 – 28	106°25'30"	100,08
28 – 29	351°12'30"	210,86
29 – 30	41°13'17"	99,09
30 – 05	149°44'42"	16,73
05 – 04	41°44'42"	188,85
04 – 03	307°17'21"	88,54
03 – 02	308°13'52"	172,62

ÁREA = 205.016,95 m2

PONTO	AZIMUTE	DISTÂNCIA
30 – 31	342°36'01"	351,25
31 – A	29°34'47"	20,52
A – B	162°36'01"	344,32
B – 30	198°13'57"	25,75

ÁREA = 5.216,76 m2

CURVAS	CORDA	ANG.CENTRAL	RAIO	DESENV.	TANG.
C1	9,18	54°37'25"	10,00	9,53	5,16
C2	8,26	54°37'25"	9,00	8,58	4,65
C3	7,95	46°49'40"	10,00	8,17	4,33
C4	7,15	46°49'35"	9,00	7,36	3,90
C5	36,68	4°26'52"	472,64	36,69	18,35
C6	38,08	4°26'52"	490,64	38,09	19,05
C7	17,95	96°49'14"	12,00	20,28	13,52
C8	21,24	83°10'46"	16,00	23,23	14,20
C9	60,95	27°19'41"	129,00	61,53	31,36
C10	52,44	27°19'41"	111,00	52,94	26,99
C11	30,89	20°05'23"	88,55	31,05	15,69
C12	37,17	20°05'23"	106,55	37,36	18,87
C13	6,15	11°45'36"	30,00	6,16	3,09
C14	6,15	11°45'36"	30,00	6,16	3,09
C15	13,96	101°45'36"	9,00	15,98	11,07
C16	12,73	90°00'00"	9,00	14,14	9,00
C17	12,73	90°00'00"	9,00	14,14	9,00
C18	12,73	90°00'00"	9,00	14,14	9,00
C19	24,95	57°20'55"	26,00	26,02	14,22
C20	38,39	57°20'56"	40,00	40,04	21,88
C21	8,77	122°39'04"	5,00	10,70	9,14
C22	22,07	57°20'56"	23,00	23,02	12,58
C23	57,86	64°47'01"	54,00	61,06	34,26
C24	42,86	64°47'01"	40,00	45,23	25,38
C25	12,46	87°35'10"	9,00	13,76	8,63
C26	12,99	92°24'50"	9,00	14,52	9,39
C27	19,11	44°57'05"	25,00	19,61	10,34
C28	7,39	135°02'55"	4,00	9,43	9,67
C29	7,45	137°21'55"	4,00	9,59	10,25
C30	12,46	87°35'10"	9,00	13,76	8,63
C31	12,99	92°24'50"	9,00	14,52	9,39
C32	16,72	42°38'05"	23,00	17,11	8,98
C33	12,46	87°35'10"	9,00	13,76	8,63
C34	31,83	87°35'10"	23,00	35,16	22,05
C35	7,45	137°21'55"	4,00	9,59	10,25
C36	16,72	42°38'05"	23,00	17,11	8,98
C37	24,23	23°17'36"	60,00	24,39	12,37
C38	18,57	23°17'36"	46,00	18,70	9,48
C39	19,88	19°04'19"	60,00	19,97	10,08
C40	24,52	19°04'19"	74,00	24,63	12,43
C41	12,73	90°00'00"	9,00	14,14	9,00
C42	12,73	90°00'00"	9,00	14,14	9,00
C43	11,42	144°22'04"	6,00	15,12	18,67
C44	11,01	35°37'56"	18,00	11,19	5,78
C45	8,90	125°37'56"	5,00	10,96	9,74
C46	11,69	14°36'20"	46,00	11,73	5,89
C47	11,52	127°52'57"	6,42	14,30	13,04
C48	7,91	46°35'12"	10,00	8,13	4,31
C49	27,60	26°35'41"	60,00	27,85	14,18
C50	32,83	18°53'53"	100,00	32,98	16,64
C51	21,35	20°23'05"	60,00	21,35	10,79
C52	18,40	26°35'41"	40,00	18,57	9,45

FUNDOS		LATERAL DIREITA		LATERAL ESQUERDA	
LOTES	QUADRA	LOTES	QUADRA	LOTES	QUADRA
12 ao 18	D			10	D
20 ao 24	D				
03 e 04	G				
06 e 07	G				
03 ao 13	H				

IDENTIFICAÇÃO	PERÍMETRO (m) FRENTE	DIREITA	ESQUERDA	FUNDOS	ÁREA (m2)
LOTE 10 – QD "D"	2,00	21,67	21,50	2,01	43,17
LOTE 12 – QD "D"	10,00	3,00	3,00	10,00	30,00
LOTE 13 – QD "D"	10,00	3,00	3,00	10,00	30,00
LOTE 14 – QD "D"	10,00	3,00	3,00	10,00	30,00
LOTE 15 – QD "D"	10,00	3,00	3,00	10,00	30,00
LOTE 16 – QD "D"	10,00	3,00	3,00	10,00	30,00
LOTE 17 – QD "D"	10,00	3,00	3,00	10,00	30,00
LOTE 18 – QD "D"	10,00	3,00	3,00	10,00	30,00
LOTE 20 – QD "D"	10,00	3,00	3,00	10,00	30,00
LOTE 21 – QD "D"	10,00	3,00	3,00	10,00	30,00
LOTE 22 – QD "D"	10,00	3,00	3,00	10,00	30,00
LOTE 23 – QD "D"	10,50	3,00	3,00	10,50	31,50
LOTE 24 – QD "D"	19,06	3,56	3,00	20,98	60,06
LOTE 03 – QD "H"	10,00	3,00	3,00	10,00	30,00
LOTE 04 – QD "H"	10,00	3,00	3,00	10,00	30,00
LOTE 06 – QD "H"	10,00	3,00	3,00	10,00	30,00
LOTE 07 – QD "H"	7,09	4,24	3,00	4,09	16,78
LOTE 03 – QD "H"	10,00	3,00	3,00	10,00	30,00
LOTE 04 – QD "H"	10,00	3,00	3,00	10,00	30,00
LOTE 05 – QD "H"	10,00	3,00	3,00	10,00	30,00
LOTE 06 – QD "H"	10,00	3,00	3,00	10,00	30,00
LOTE 07 – QD "H"	10,00	3,00	3,00	10,00	30,00
LOTE 08 – QD "H"	10,00	3,00	3,00	10,00	30,00
LOTE 09 – QD "H"	10,00	3,00	3,00	10,00	30,00
LOTE 10 – QD "H"	10,00	3,00	3,00	10,00	30,00
LOTE 11 – QD "H"	10,00	3,00	3,00	10,00	30,00
LOTE 12 – QD "H"	11,38	3,00	3,00	11,38	34,14
LOTE 13 – QD "H"	3,26	----	3,00	4,43	4,88

QUADRO DE ÁREAS AUXILIAR			
ESPECIFICAÇÃO		ÁREAS(m2)	%
LOTES		78.302,28 274 LOTES	38,19
QUADRA A (10 LOTES)	6.072,61 m2		
QUADRA B (33 LOTES)	9.632,51 m2		
QUADRA C (09 LOTES)	2.285,11 m2		
QUADRA D (38 LOTES)	9.928,64 m2		
QUADRA E (17 LOTES)	4.442,26 m2		
QUADRA F (32 LOTES)	8.769,06 m2		
QUADRA G (8 LOTES)	2.684,41 m2		
QUADRA H (21 LOTES)	5.752,67 m2		
QUADRA I (50 LOTES)	13.628,12 m2		
QUADRA J (22 LOTES)	5.633,46 m2		
QUADRA K (12 LOTES)	3.533,51 m2		
QUADRA L (22 LOTES)	5.939,92 m2		
RUAS		50.799,48	24,78
AVENIDA 01	10.706,22 m2		
RUA 01	14.835,75 m2		
RUA 02	1.122,43 m2		
RUA 03	1.276,04 m2		
RUA 04	2.455,75 m2		
RUA 05	3.805,32 m2		
RUA 06	728,55 m2		
RUA 07	3.003,09 m2		
RUA 08	1.296,76 m2		
RUA 09	3.090,12 m2		
RUA 10	1.227,95 m2		
VIELA 01	150,00 m2		
VIELA 02	321,15 m2		
VIELA 03	100,00 m2		
FAIXA NÃO EDIFICANTE DESTINADA AO SISTEMA VIÁRIO Diretriz Viária Municipal Definida no Plano Diretor Lei nº 7.858/12 e Processos de Diretrizes nº's 31.519–8/2015 e 4.528–0/2016	5.216,76 m2		
FAIXA DESTINADA AO SISTEMA VIÁRIO/ AVENIDA MARGINAL Diretriz Viária Municipal Definida no Plano Diretor Lei nº 7.858/12 e Processos de Diretrizes nº's 31.519–8/2015 e 4.528–0/2016	1.463,59 m2		
ÁREAS VERDES		53.901,90	26,29
ÁREA VERDE 01	2.435,44 m2		
ÁREA VERDE 02	9.304,32 m2		
ÁREA VERDE 03	28.997,60 m2		
ÁREA VERDE 04	12.720,45 m2		
ÁREA VERDE 05	444,09 m2		
ÁREA INSTITUCIONAL (EQUIPAMENTO URBANO E COMUNITÁRIO)			
ÁREA INSTITUCIONAL	10.528,74 m2	10.899,03	5,32
ÁREA INSTITUCIONAL ESPECIAL (DESTINADA A IMPLANTAÇÃO DA ESTAÇÃO ELEVATÓRIA DE ESGOTO)	370,29 m2		
SISTEMA DE LAZER		11.114,26	5,42
SISTEMA DE LAZER 01	8.384,72 m2		
SISTEMA DE LAZER 02	1.222,75 m2		
SISTEMA DE LAZER 03	720,38 m2		
SISTEMA DE LAZER 04	786,41 m2		
TOTAL		205.016,95	100,00

QUADRO DE ÁREAS			
ESPECIFICAÇÃO		ÁREAS(m2)	%
1.	ÁREA DOS LOTES (274)	78.302,28	38,19
2.	TOTAL DE ÁREAS PÚBLICAS	126.714,67	61,81
2.1.	SISTEMA VIÁRIO	50.799,48	24,78
2.2.	ÁREAS INSTITUCIONAIS (EQUIPAMENTOS URBANOS E COMUNITÁRIOS)	10.899,03	5,32
2.3.	ÁREAS LIVRES DE USO PÚBLICO	65.016,16	31,71
2.3.1	ÁREAS VERDES	53.901,90	26,29
2.3.2	SISTEMAS DE LAZER	11.114,26	5,42
3.	OUTROS	---	---
4.	ÁREA TOTAL LOTEADA	205.016,95	100,00
5.	ÁREA REMANESCENTE	---	---
6.	TOTAL DA GLEBA	205.016,95	---
2.3.1	ÁREA VERDE	53.901,90	26,29
2.3.1.1	ÁREA VERDE FORA DE A.P.P.	20.810,17	10,15
2.3.1.2	ÁREA VERDE DENTRO DE A.P.P.	33.091,73	16,14