DETALHE - Passagem de fauna subterrânea (Projetada)

Aduelas de Concreto 3,00 x 2,00 m, Tubos Celulares, pré-moldadas (40,00 metros)

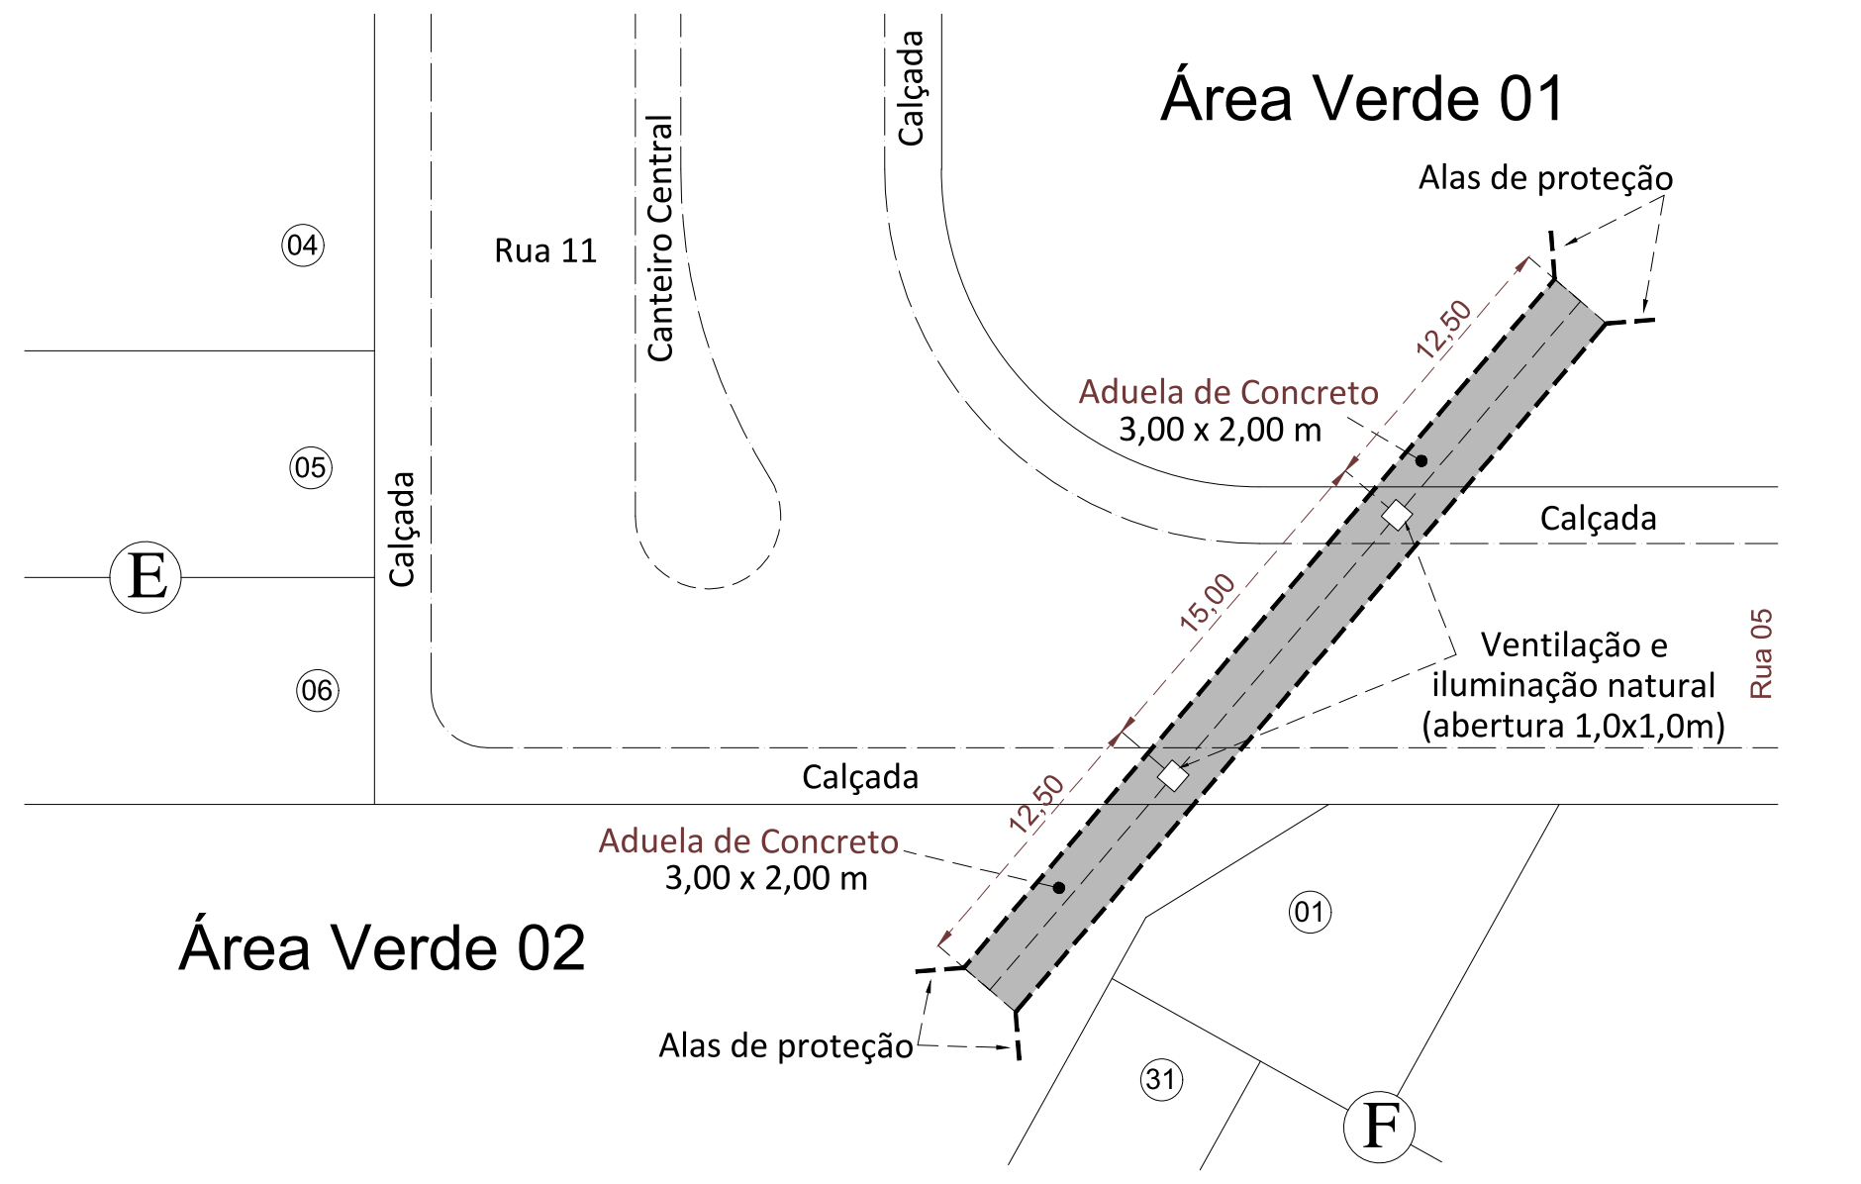

Área Verde 01
Alas de proteção
Rua 11
Canteiro Central
Calçada
04
05
06
E
Aduela de Concreto
3,00 x 2,00 m
12,50
15,00
12,50
Calçada
Ventilação e
iluminação natural
(abertura 1,0x1,0m)
Rua 05
Calçada
Aduela de Concreto
3,00 x 2,00 m
Área Verde 02
Alas de proteção
01
31
F

Obs:
1) Será executada passagem aérea junto da passagem subterrânea, conforme Relatório Técnico Ambiental.
2) Fechamento com cercas/alambrados, ao longo da rodovia, áreas verdes com Ruas e lotes

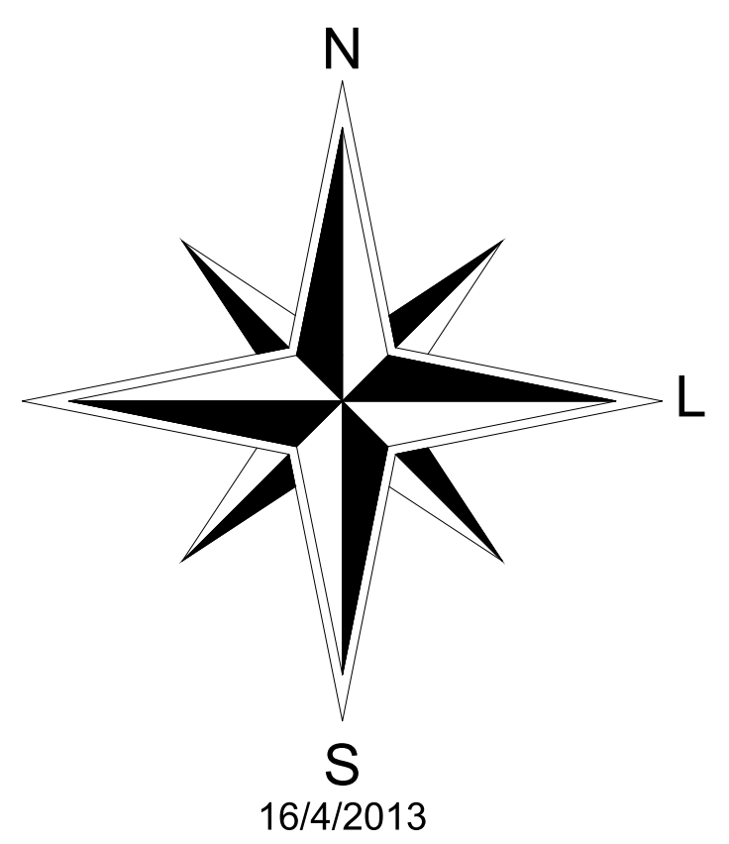

16/4/2013

Sistema de Coordenadas:
Coordenadas Planas, Sistema UTM
Datum: SIRGAS 2000
Origem das coordenadas:
N = Equador acrescido de 10.000.000,00 m
E = MC 45° acrescido de 500.000,00 m

Escala Nominal = 1 : 1.000
Escala Gráfica

0m 10 20 30 40 50 60 80 100

SITUAÇÃO 1/ 10.000

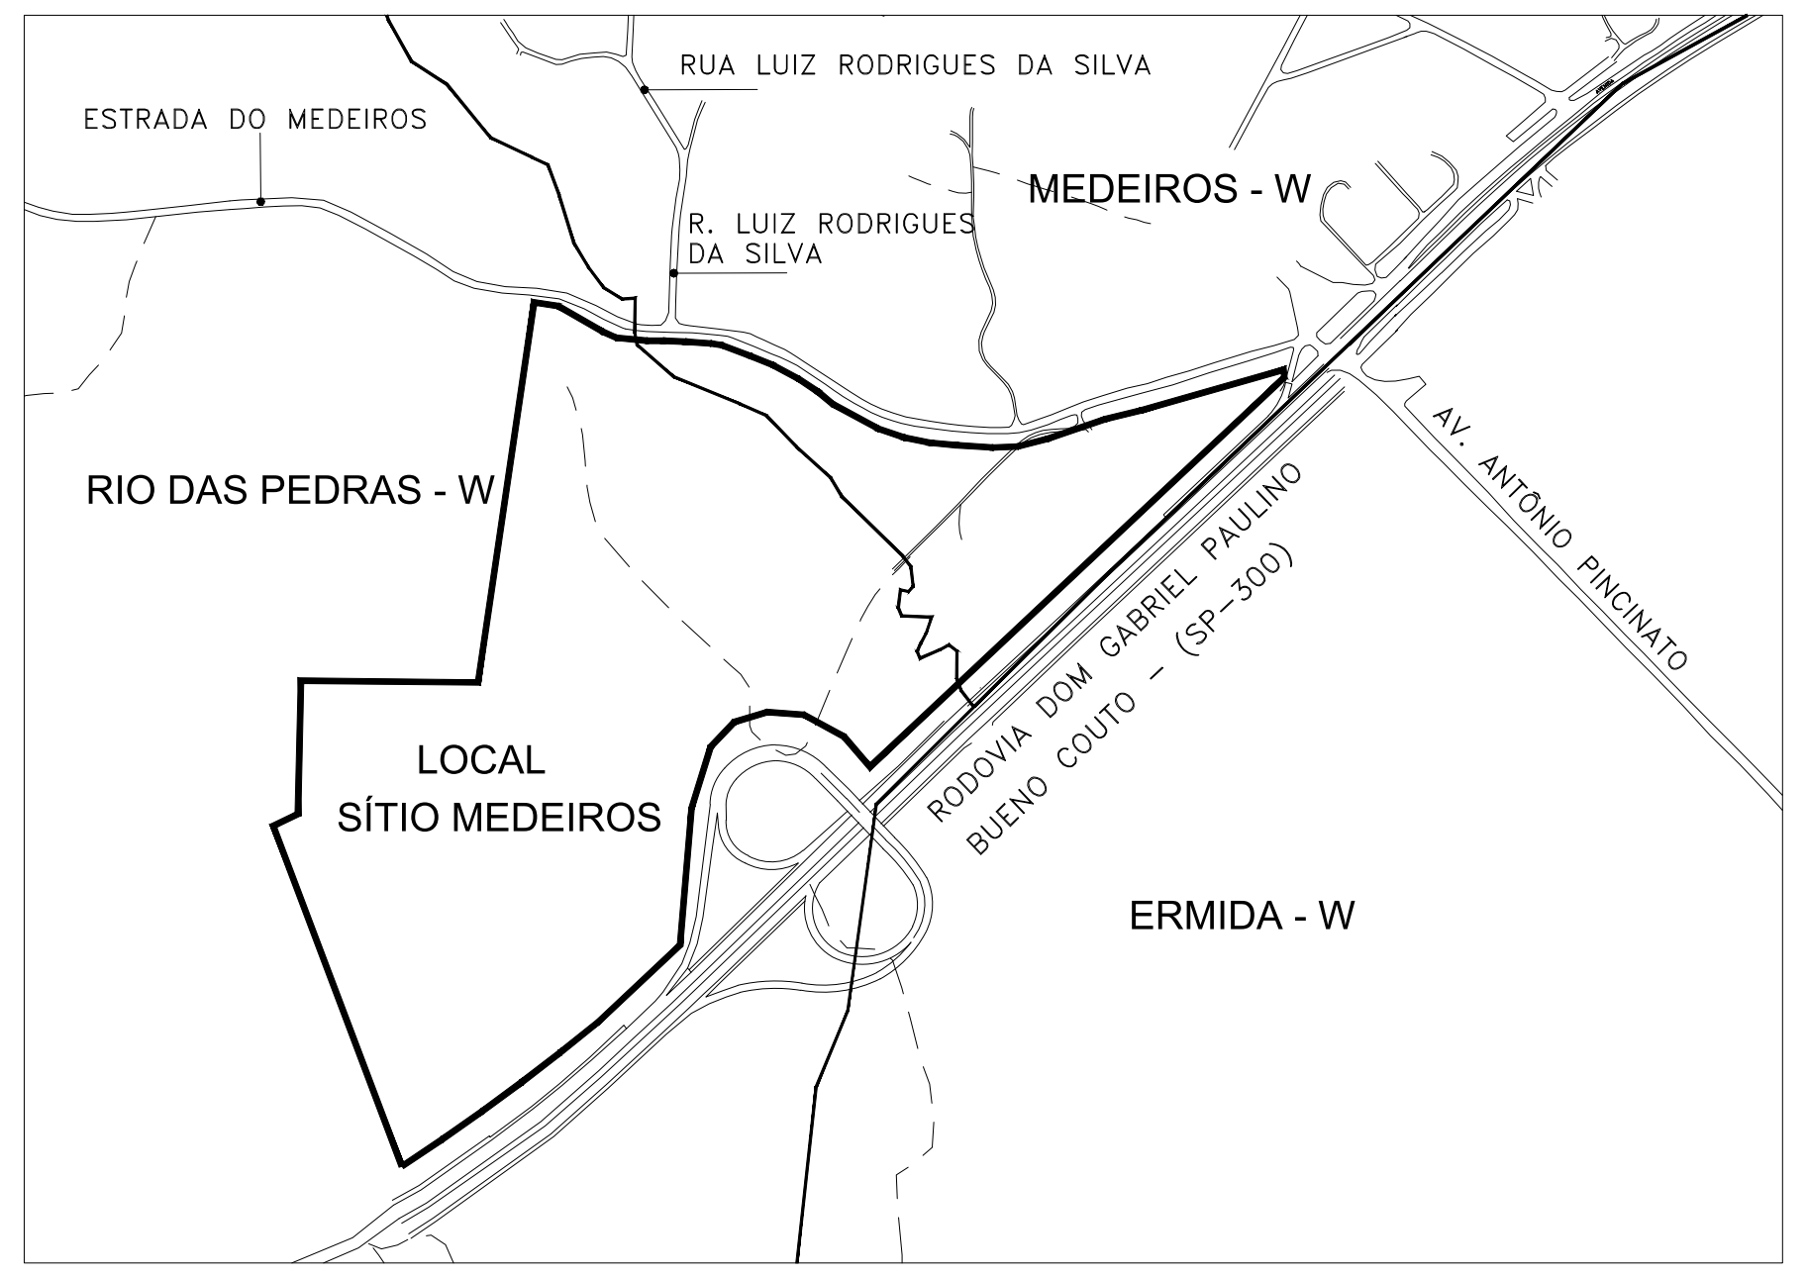

RUA LUIZ RODRIGUES DA SILVA
ESTRADA DO MEDEIROS
R. LUIZ RODRIGUES DA SILVA
MEDEIROS - W
RIO DAS PEDRAS - W
LOCAL
SÍTIO MEDEIROS
RODOVIA DOM GABRIEL PAULINO BUENO COUTO - (SP-300)
AV. ANTÔNIO PINCINATO
ERMIDA - W

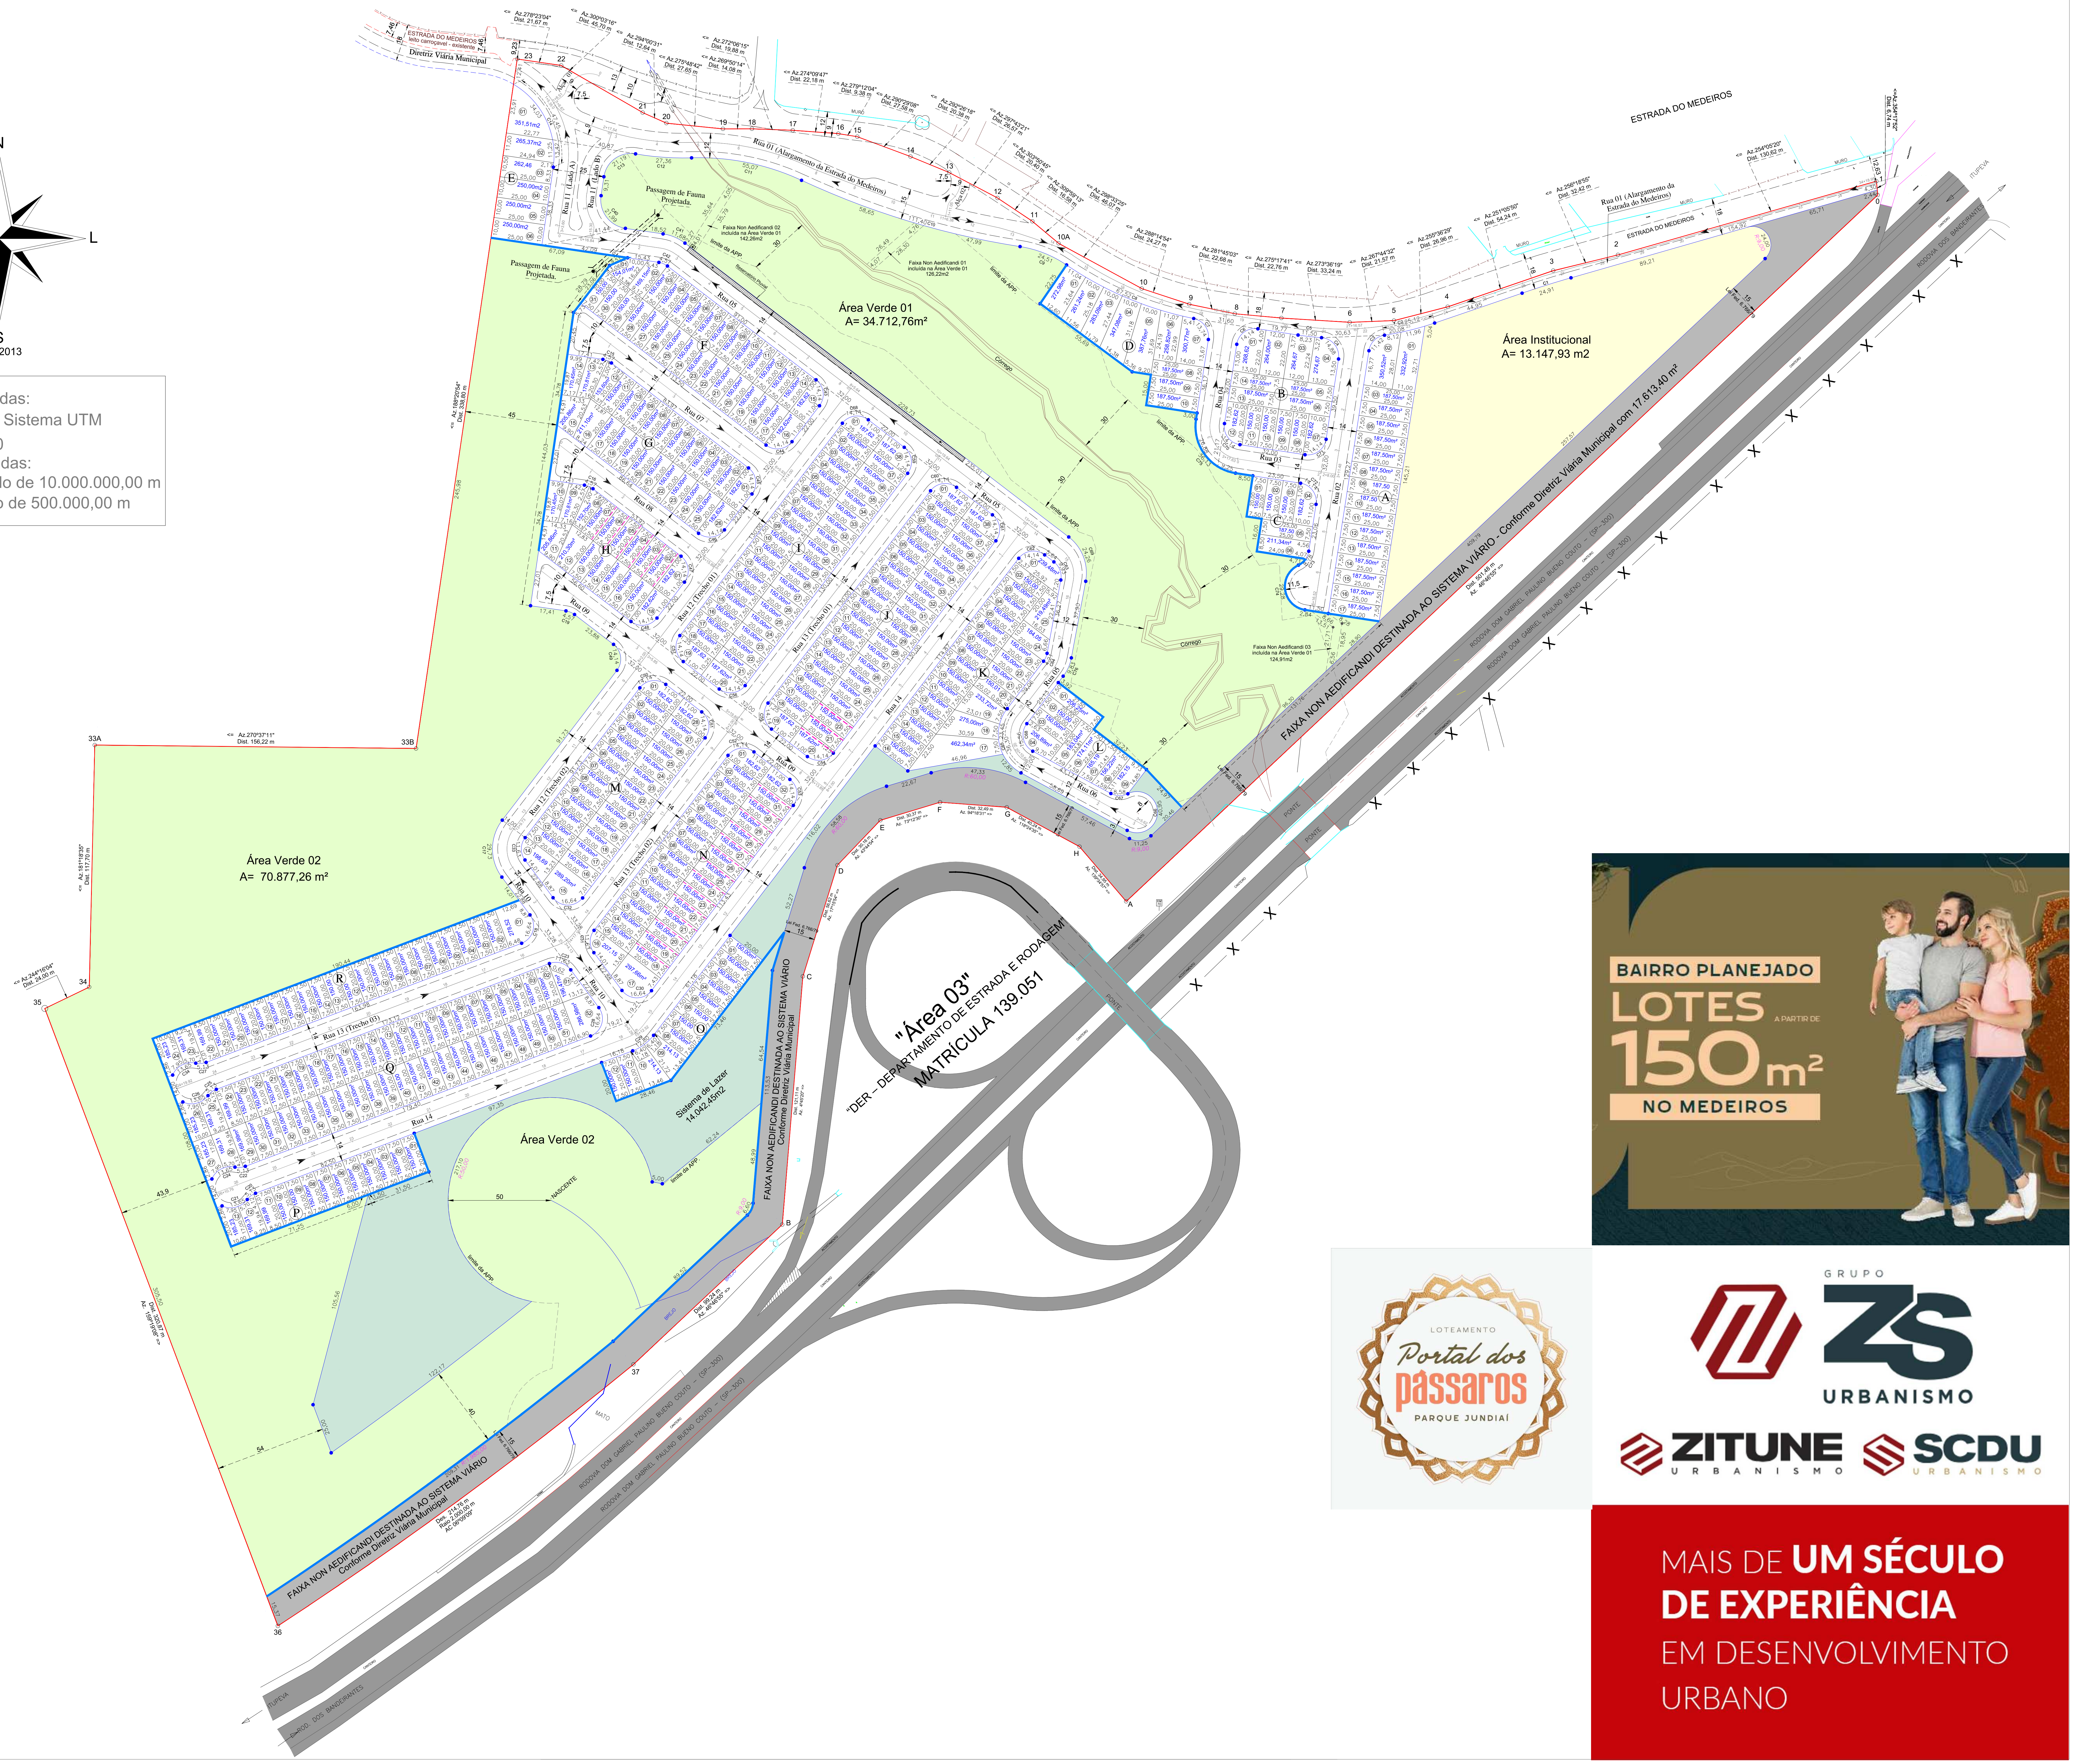

ESTRADA DO MEDEIROS
Diretriz Viária Municipal
Rua 01 (Alargamento da Estrada do Medeiros)
Passagem de Fauna Projetada.
Área Verde 01
A= 34.712,76m²
Área Institucional
A= 13.147,93 m2
FAIXA NON AEDIFICANDI DESTINADA AO SISTEMA VIÁRIO - Conforme Diretriz Viária Municipal com 17.613,40 m²
Faixa Non Aedificandi 03
incluída na Área Verde 01
124,91m2
Córrego
Rua 02
Rua 03
Rua 04
Rua 10
Rua 13 (Trecho 02)
Rua 14
Área Verde 02
A= 70.877,26 m²
Área Verde 02
Sistema de Lazer
14.042,45m2
limite da APP.
"Área 03"
"DER – DEPARTAMENTO DE ESTRADA E RODAGEM"
MATRÍCULA 139.051
FAIXA NON AEDIFICANDI DESTINADA AO SISTEMA VIÁRIO
Conforme Diretriz Viária Municipal
Lei Fed. 6.766/79
RODOVIA DOM GABRIEL PAULINO BUENO COUTO - (SP-300)
PONTE
ACOSTAMENTO
CANTEIRO
A
B
C
D
E
F
G
H
I
J
K
L
M
N
O
P
Q
R

LEGENDA

- ☐ Lotes Residenciais
- 🟨 Área Institucional
- 🟩 Áreas Verdes
- 🟩 Sistema de Lazer
- ▨ FAIXA NON AEDIFICANDI DESTINADA AO SISTEMA VIÁRIO Conforme Diretriz Viária Municipal
- ☐ Faixas Non Aedificandis para implantação de infraestrutura
- ▨ Vias Externas existentes
- — Alambrado
- ☐ Faixas non aedificandis permeáveis nos lotes

BAIRRO PLANEJADO
LOTES A PARTIR DE 150m²
NO MEDEIROS

LOTEAMENTO
Portal dos passaros
PARQUE JUNDIAÍ

GRUPO ZS URBANISMO

ZITUNE URBANISMO

SCDU URBANISMO

MAIS DE UM SÉCULO DE EXPERIÊNCIA EM DESENVOLVIMENTO URBANO